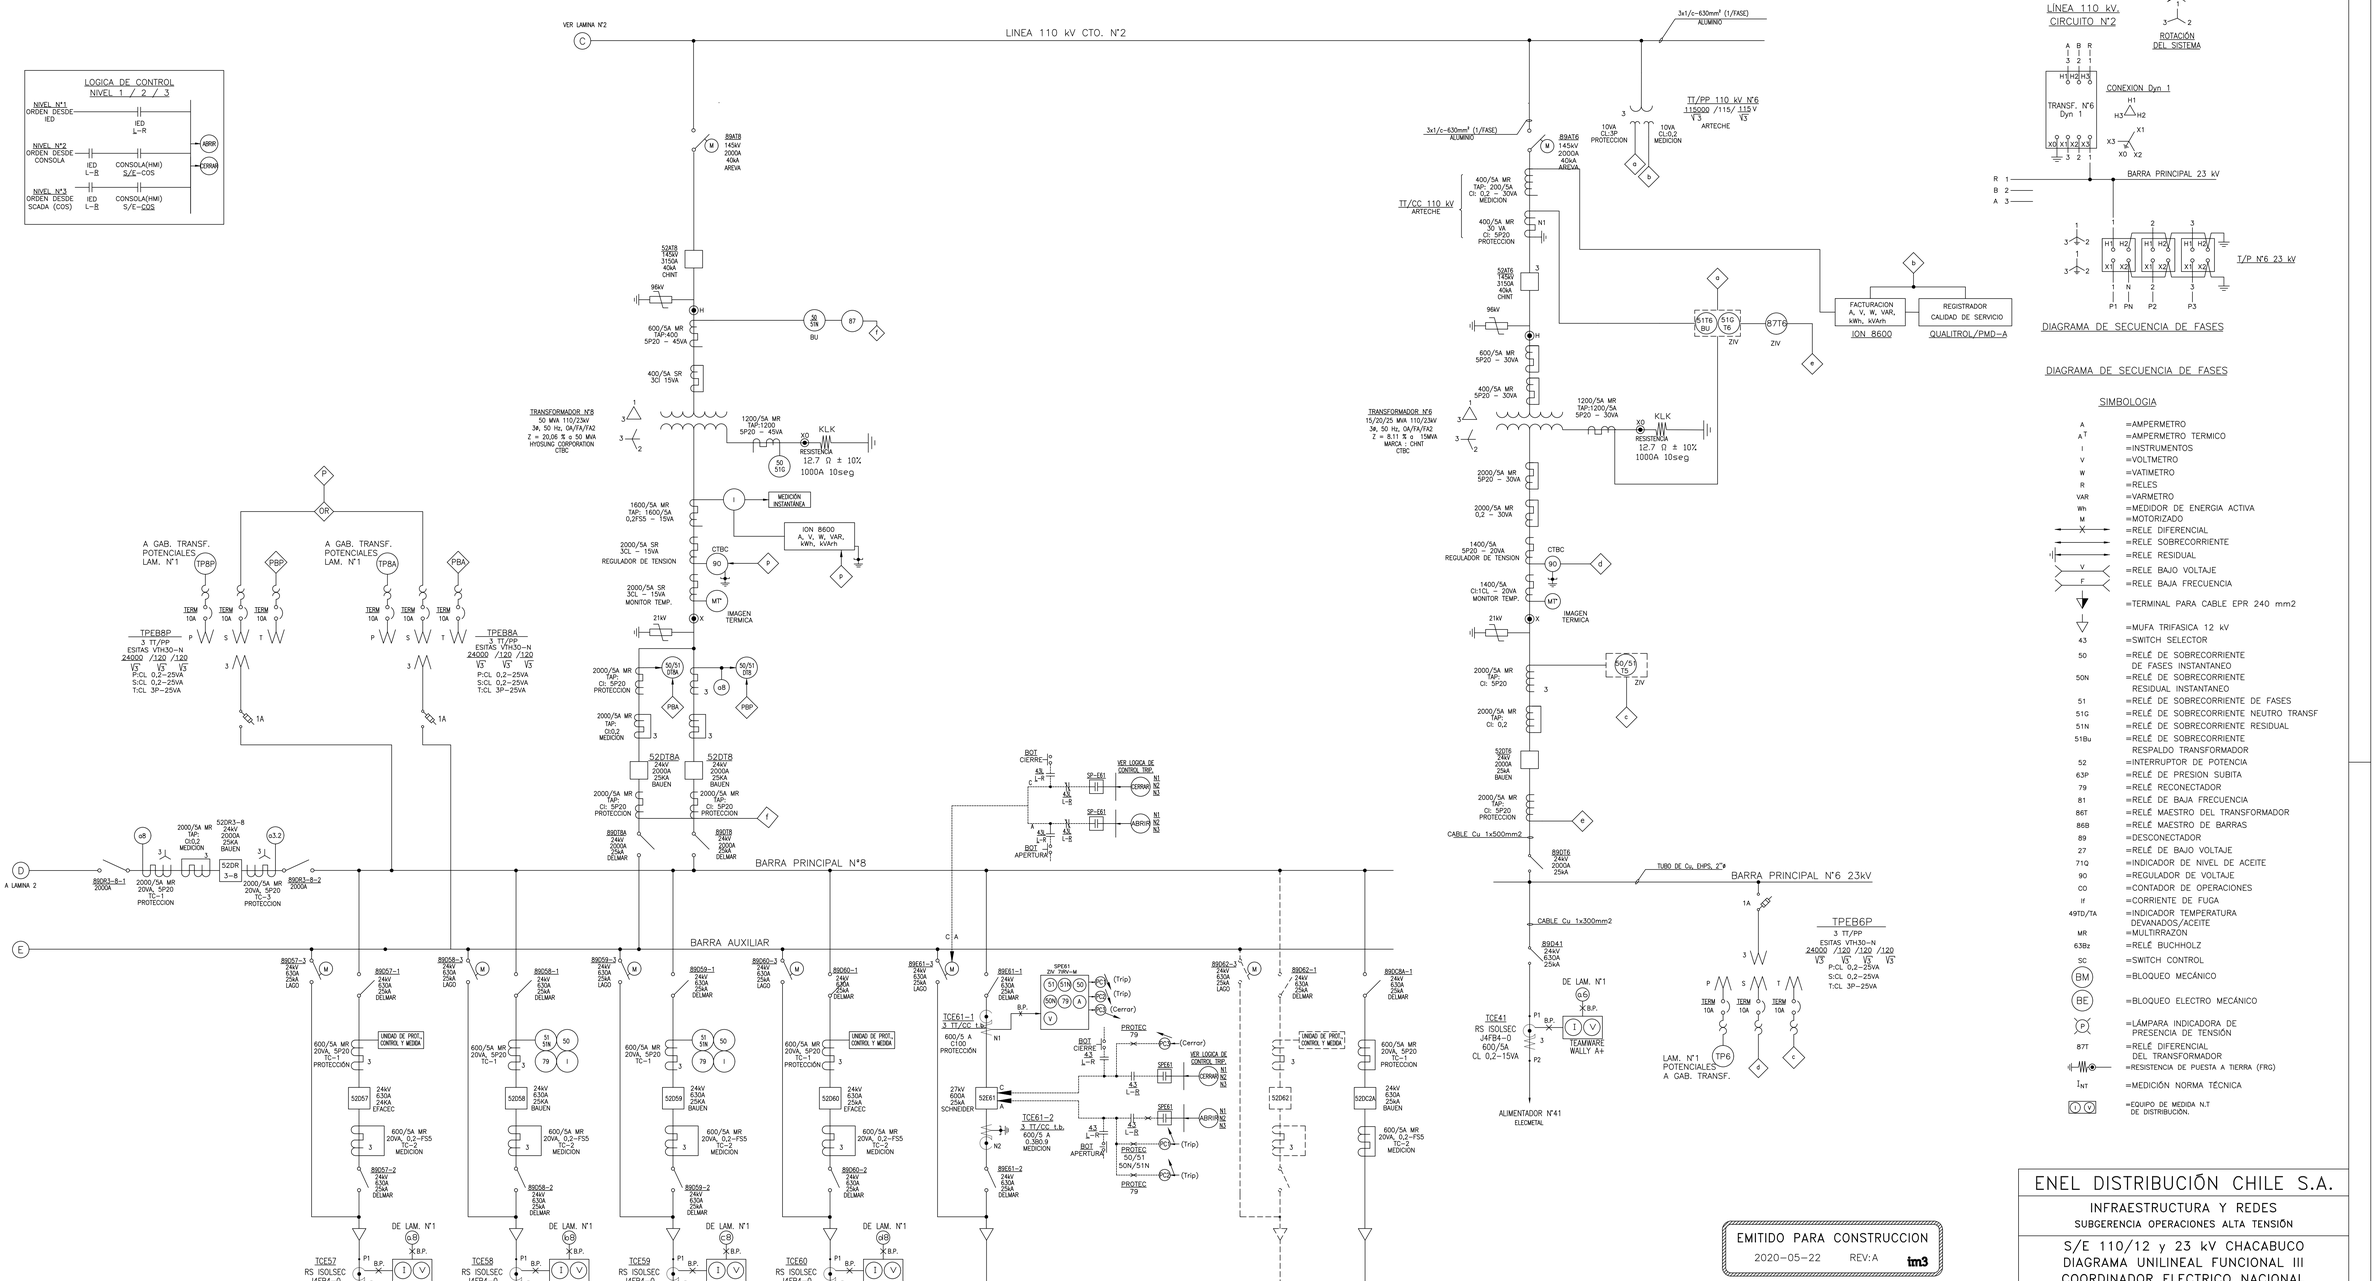


SIMBOLOGIA

A	=AMPERMETRO
A^T	=AMPERMETRO TERMICO
I	=INSTRUMENTOS
V	=VOLTMETRO
W	=VATIMETRO
R	=RELES
VAR	=VARMETRO
Wh	=MEDIDOR DE ENERGIA ACTIVA
M	=MOTORIZADO
X	=RELE DIFERENCIAL
	=RELE SOBRECORRIENTE
	=RELE RESIDUAL
V	=RELE BAJO VOLTAJE
F	=RELE BAJA FRECUENCIA
	=TERMINAL PARA CABLE EPR 240 mm2
	=MUFA TRIFASICA 12 kV
43	=SWITCH SELECTOR
50	=RELÉ DE SOBRECORRIENTE DE FASES INSTANTANEO
50N	=RELÉ DE SOBRECORRIENTE RESIDUAL INSTANTANEO
51	=RELÉ DE SOBRECORRIENTE DE FASES
51G	=RELÉ DE SOBRECORRIENTE NEUTRO TRANSF
51N	=RELÉ DE SOBRECORRIENTE RESIDUAL
51Bu	=RELÉ DE SOBRECORRIENTE RESPALDO TRANSFORMADOR
52	=INTERRUPTOR DE POTENCIA
63P	=RELÉ DE PRESION SUBITA
79	=RELÉ RECONECTADOR
81	=RELÉ DE BAJA FRECUENCIA
86T	=RELÉ MAESTRO DEL TRANSFORMADOR
86B	=RELÉ MAESTRO DE BARRAS
89	=DESCONECTADOR
27	=RELÉ DE BAJO VOLTAJE
71Q	=INDICADOR DE NIVEL DE ACEITE
90	=REGULADOR DE VOLTAJE
CO	=CONTADOR DE OPERACIONES
If	=CORRIENTE DE FUGA
49TD/TA	=INDICADOR TEMPERATURA DEVANADOS/ACEITE
MR	=MULTIRRAZON
63Bz	=RELÉ BUCHHOLZ
SC	=SWITCH CONTROL
BM	=BLOQUEO MECÁNICO
BE	=BLOQUEO ELECTRO MECÁNICO
P	=LÁMPARA INDICADORA DE PRESENCIA DE TENSIÓN
87T	=RELÉ DIFERENCIAL DEL TRANSFORMADOR
	=RESISTENCIA DE PUESTA A TIERRA (FRG)
I_{NT}	=MEDICIÓN NORMA TÉCNICA
I V	=EQUIPO DE MEDIDA N.T DE DISTRIBUCIÓN.

EMITIDO PARA CONSTRUCCION
2020-05-22 REV:A tm3

ENEL DISTRIBUCIÓN CHILE S.A.
INFRAESTRUCTURA Y REDES
SUBGERENCIA OPERACIONES ALTA TENSIÓN
S/E 110/12 y 23 kV CHACABUCO
DIAGRAMA UNILINEAL FUNCIONAL III
COORDINADOR ELECTRICO NACIONAL

N°	FECHA	MODIFICACIONES	PROY.	DIB.	REV.	APROBO
5						
4						
3	22.05.20	INSTALACIÓN ALIMENTADOR N°61 – 23kV TR8	IM3	IM3	G.C.C.	M.C.
2	03.02.20	ADECUACIÓN POR NORMA TÉCNICA DE DISTRIBUCIÓN	I–SEP	I–SEP	N.V.S.	UDOAT
1	30.11.18	(PROY.) INSTALACION "RPA1" TR1, TR2, TR3 Y TR6	IM.3	IM3	CMC	M.C.

ESCALA: NO | CHI-28931-003
PROYECTO: IM3
DIBUJO: IM3
REVISO: G. CANDIA C.
JEFE UNIDAD: M. GONZALEZ C.
UNIDAD APROB.: UDOAT

APROBADO | FECHA:
JEFE UNIDAD

CHI-28931
LAMINA 3 de 4