



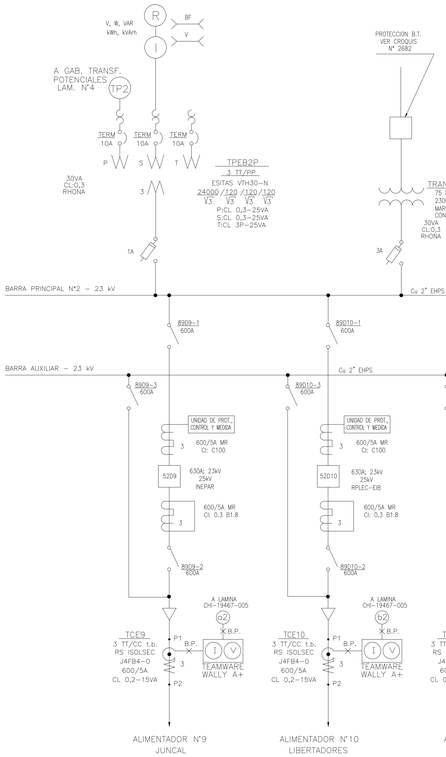


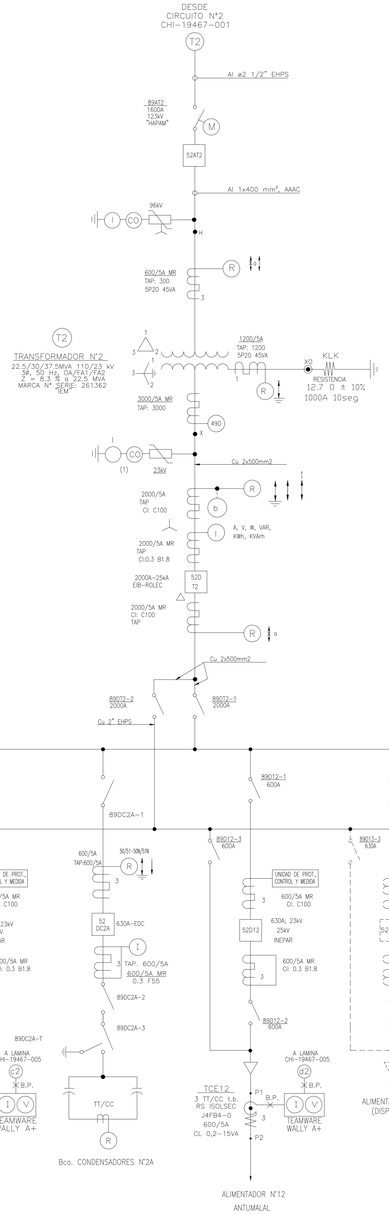

SIMBOLOGIA:

A	=	AMPERMETRO
A'	=	AMPERMETRO TERMICO
I	=	INSTRUMENTOS
V	=	VOLTMETRO
W	=	VATMETRO
R	=	RELES
VAR	=	VARMETRO
Wh	=	MEDIDOR DE ENERGIA ACTIVA
M	=	MOTORIZADO
	=	TERMINAL PARA CABLE EPR 240 mm2
	=	MUFA TRIFASICA 12 kV
27	=	RELÉ DE BAJO VOLTAJE
43	=	SWITCH SELECTOR
49TD/TA	=	INDICADOR TEMPERATURA DEVANADOS/ACEITE
50	=	RELÉ DE SOBRECORRIENTE DE FASES INSTANTANEO
50N	=	RELÉ DE SOBRECORRIENTE RESIDUAL INSTANTANEO
51	=	RELÉ DE SOBRECORRIENTE DE FASES
51G	=	RELÉ DE SOBRECORRIENTE NEUTRO TRANSF.
51N	=	RELÉ DE SOBRECORRIENTE RESIDUAL
51Bu	=	RELÉ DE SOBRECORRIENTE RESPALDO TRANSFORMADOR
52	=	INTERRUPTOR DE POTENCIA
63P	=	RELÉ DE PRESION SUBITA
63Bz	=	RELÉ BUCHHOLZ
71Q	=	INDICADOR DE NIVEL DE ACEITE
79	=	RELÉ RECONECTADOR
81	=	RELÉ DE BAJA FRECUENCIA
86T	=	RELÉ MAESTRO DEL TRANSFORMADOR
86B	=	RELÉ MAESTRO DE BARRAS
87T	=	RELÉ DIFERENCIAL DEL TRANSFORMADOR
89	=	DESCONECTADOR
90	=	REGULADOR DE VOLTAJE
CO	=	CONTADOR DE OPERACIONES
If	=	CORRIENTE DE FUGA
MR	=	MULTIRRAZON
SC	=	SWITCH CONTROL
BP	=	BLOQUE DE PRUEBAS
FT	=	SWITCH DE PRUEBAS
BM	=	BLOQUEO MECÁNICO
BE	=	BLOQUEO ELECTRO MECÁNICO
P	=	LÁMPARA INDICADORA DE PRESENCIA DE TENSIÓN
	=	RESISTENCIA DE PUESTA A TIERRA (FRG)
	=	MEDICIÓN NORMA TÉCNICA
	=	EQUIPO DE MEDIDA N.T. DE DISTRIBUCIÓN.

LOGICA DE CONTROL
NIVEL 1 / 2 / 3

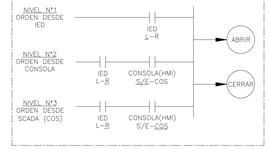

TRANSFORMADOR DE CORRIENTE MULTI RAZON TABLA 1							
600:5	50:5 100:5 150:5 200:5 250:5 300:5 400:5 450:5 500:5 600:5	1200:5	100:5 200:5 300:5 400:5 500:5 600:5 800:5 900:5 1000:5 1200:5	2000:5	300:5 400:5 500:5 800:5 1100:5 1200:5 1500:5 1600:5 2000:5	3000:5	300:5 500:5 800:5 1000:5 1200:5 1500:5 2000:5 2200:5 2500:5 3000:5

SEGUN NORMA ANSI/IEEE C57.13-1993

REFERENCIAS:

CHI-19468 DISPOSICIÓN GENERAL EQUIPO ELÉCTRICO – PLANTA.
CHI-19469 DISPOSICIÓN GENERAL EQUIPO ELÉCTRICO – SECCIONES.

NOTAS:

1.– EL TAP CHACABUCO INICIALMENTE SE CONECTARA A LA LINEA DE 110 kV "CERRO NAVIA – LAS VEGAS" DE GENER.

2.– EL PATIO DE 23 kV SERA PROYECTADO CONSTRUIDO PARA 6 ALIMENTADORES Y 2 BANCOS DE CONDENSADORES PARA LA ETAPA FINAL DE UN TRANSFORMADOR DE 50 MVA.

ESTE DIAGRAMA UNILINEAL REEMPLAZA AL DIAGRAMA DEL MISMO NUMERO CHI-28931 LAMINA 1 REV. 0. DE FECHA 15.05.20 ((PROY.) NT DISTRIBUCIÓN)

SOCIEDAD TRANSMISORA METROPOLITANA S.A.

GERENCIA ZONAL DE TRANSMISIÓN METROPOLITANA

ÁREA DE INGENIERÍA Y PERMISOS

SUBESTACION CHACABUCO 110/23/12kV
DIAGRAMA UNILINEAL FUNCIONAL

N°	FECHA	MODIFICACIONES	PROY	DIB.	REV.	APROB.
4	19.11.2024	HABILITACIÓN NUEVO ALIMENTADOR ASCENTY	AINAMEN	AINAMEN	H.B.N.	
3	30.07.2021	NUEVO TR4 50 MVA	IM3	IM3	N.V.S.	M.G.C.
2	30.07.2021	INSTALACIÓN TP CT5	IM3	IM3	N.V.S.	M.G.C.
1	30.07.2021	REUBICACIÓN TR4 A POSICIÓN TR5	IM3	IM3	N.V.S.	M.G.C.

ESCALA: 1:1000	STM-19467
PROYECTÓ	IM3
DIBUJÓ	IM3
REVISÓ	N. VÁSQUEZ S.
ENCARGADO	M. GONZÁLEZ C.
UNIDAD APROB.	UNIDAD APROB.
ENCARGADO DE UNIDAD	

APROBADO

FECHA: 23.05.2023

STM-19467

LÁMINA 3 DE 9