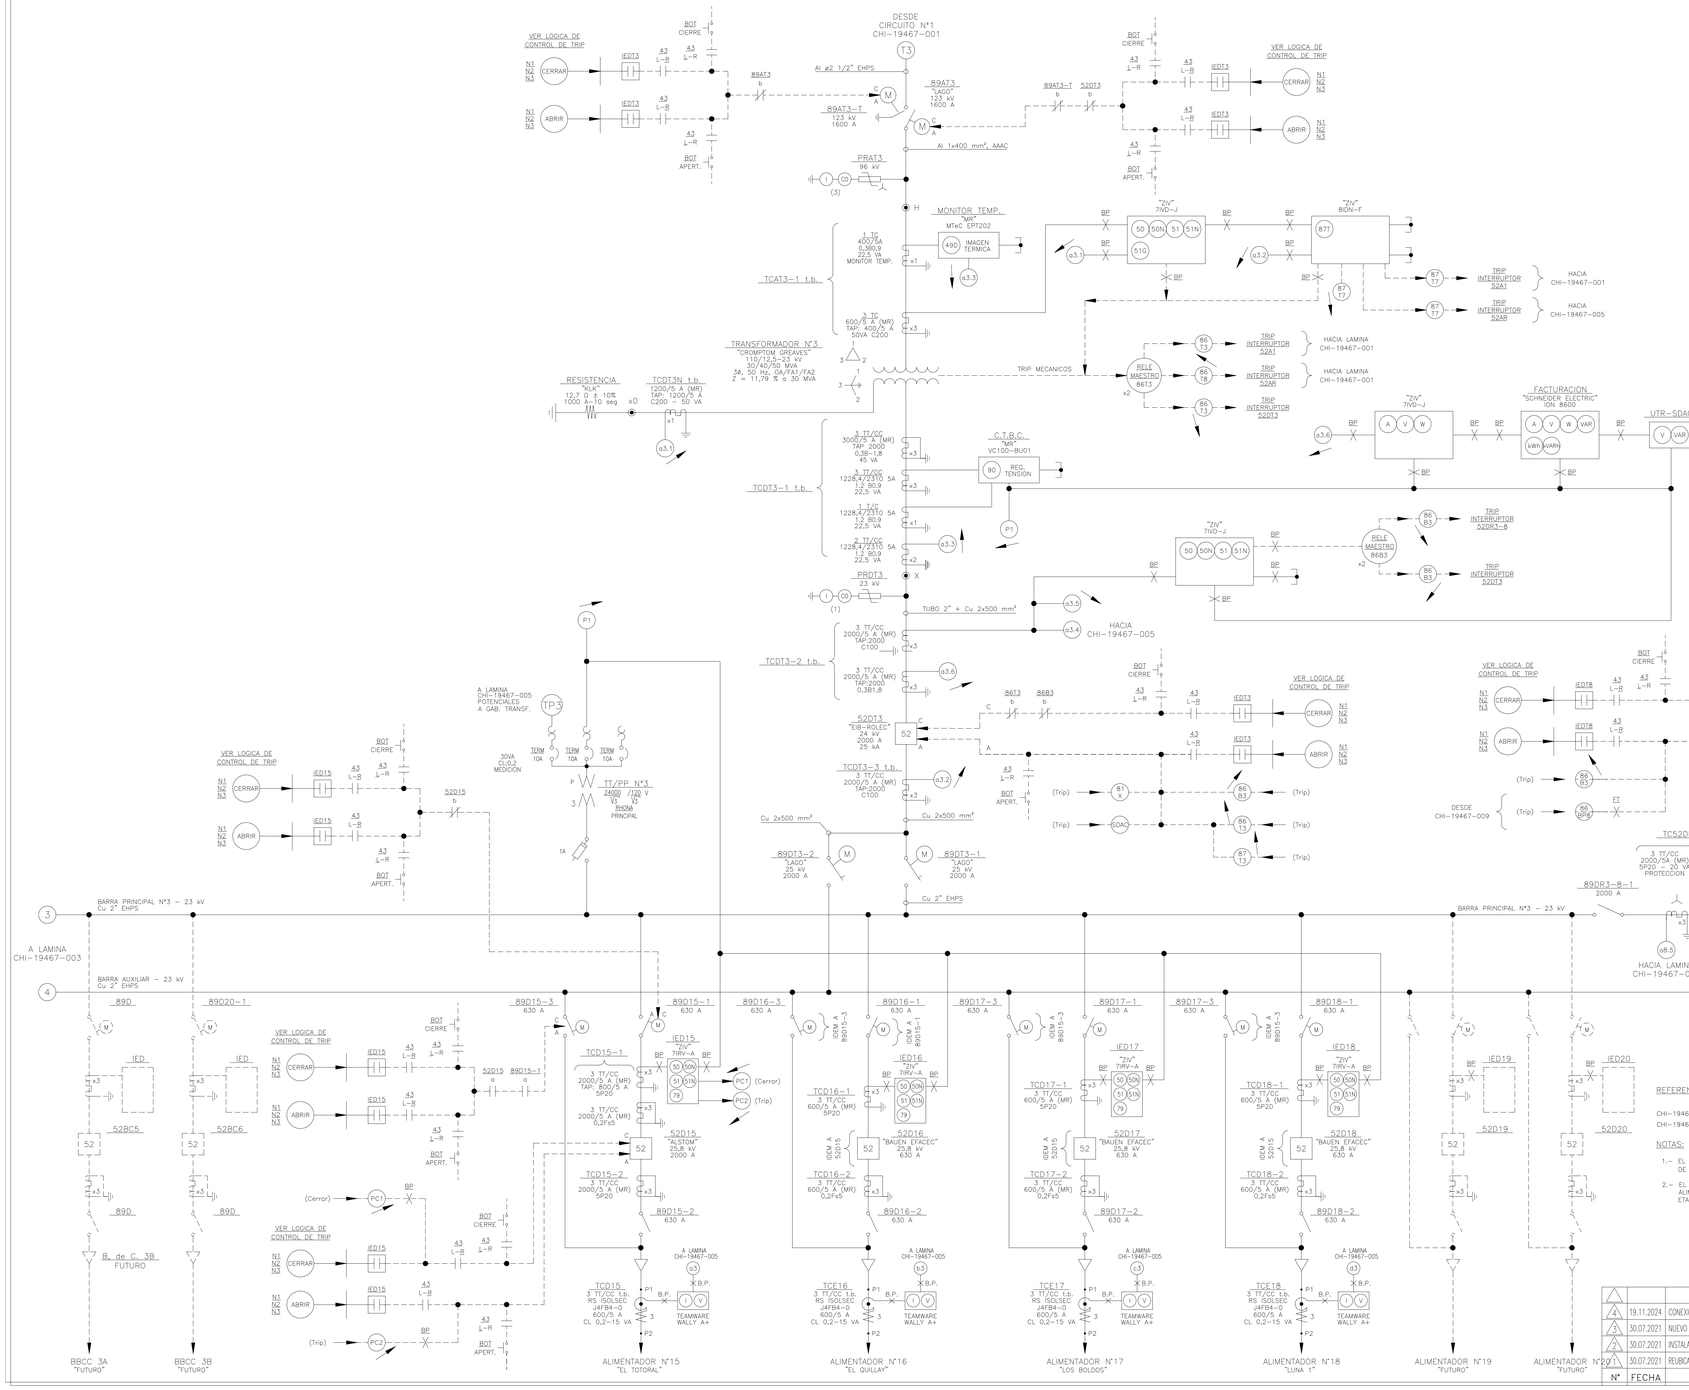


ESTE DIAGRAMA UNILINEAL REEMPLAZA AL DIAGRAMA DEL MISMO NUMERO CHI-28931 LAMINA 1 REV. 0, DE FECHA 15.05.20 ((PROY.) NT DISTRIBUCIÓN)

SOCIEDAD TRANSMISORA METROPOLITANA S.A.

GERENCIA ZONAL DE TRANSMISIÓN METROPOLITANA

ÁREA DE INGENIERÍA Y PERMISOS

SUBESTACION CHACABUCO 110/23/12kV DIAGRAMA UNILINEAL FUNCIONAL

N°	FECHA	MODIFICACIONES	PROY	DIB.	REV.	APROB.
4	19.11.2024	CONEXIÓN NUEVO ALIMENTADOR ASCENTY A PAÑO E53	ANAMEN	ANAMEN	ANAMEN	H.B.N
3	30.07.2021	NUEVO TR4 50MVA	IM.3	IM.3	N.V.S.	M.G.C.
2	30.07.2021	INSTALACIÓN TP CT5	IM.3	IM.3	N.V.S.	M.G.C.
1	30.07.2021	REUBICACIÓN TR4 A POSICIÓN TR5	IM.3	IM.3	N.V.S.	M.G.C.

ESCALA: 1:1000	STM-19467
PROYECTÓ	IM.3
DIBUJÓ	IM.3
REVISÓ	N. VÁSQUEZ S.
ENCARGADO	M. GONZÁLEZ C.
APROBADO	FECHA: 23.05.2023
ENCARGADO DE UNIDAD	LÁMINA 4 DE 9

STM-19467