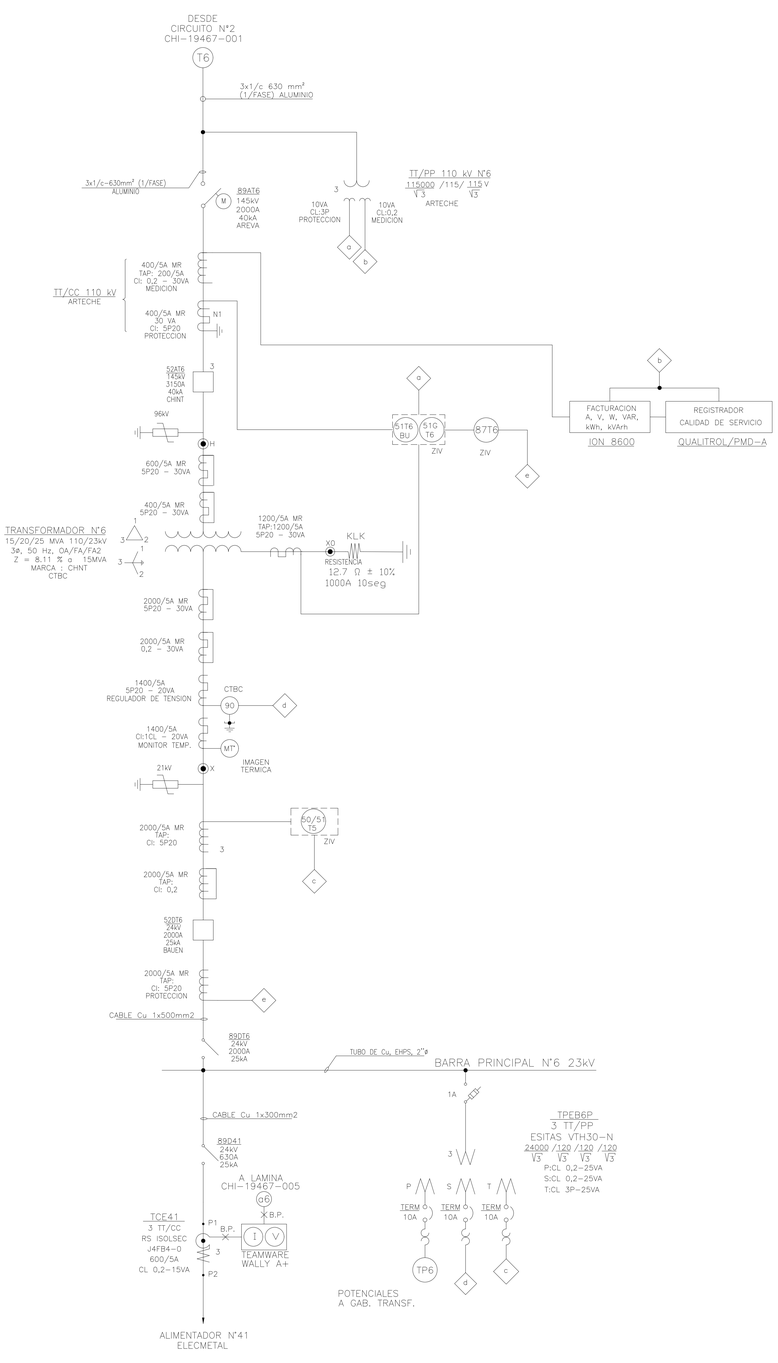



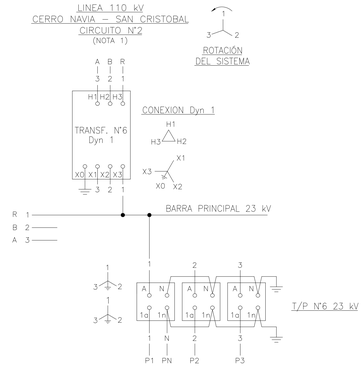


DIAGRAMA DE SECUENCIA DE FASES

SIMBOLOGIA:

A	= AMPERMETRO
A*	= AMPERMETRO TERMICO
I	= INSTRUMENTOS
V	= VOLTMETRO
W	= VATIMETRO
R	= RELES
VAR	= VARMETRO
Wh	= MEDIDOR DE ENERGIA ACTIVA
M	= MOTORIZADO
	= TERMINAL PARA CABLE EPR 240 mm2
	= MUFA TRIFASICA 12 kV
27	= RELÉ DE BAJO VOLTAJE
43	= SWITCH SELECTOR
49TD/TA	= INDICADOR TEMPERATURA DEVANADOS/ACEITE
50	= RELÉ DE SOBRECORRIENTE DE FASES INSTANTANEO
50N	= RELÉ DE SOBRECORRIENTE RESIDUAL INSTANTANEO
51	= RELÉ DE SOBRECORRIENTE DE FASES
51G	= RELÉ DE SOBRECORRIENTE NEUTRO TRANSF.
51N	= RELÉ DE SOBRECORRIENTE RESIDUAL
51Bu	= RELÉ DE SOBRECORRIENTE RESPALDO TRANSFORMADOR
52	= INTERRUPTOR DE POTENCIA
63P	= RELÉ DE PRESION SUBITA
63Bz	= RELÉ BUCHHOLZ
71Q	= INDICADOR DE NIVEL DE ACEITE
79	= RELÉ RECONECTADOR
81	= RELÉ DE BAJA FRECUENCIA
86T	= RELÉ MAESTRO DEL TRANSFORMADOR
86B	= RELÉ MAESTRO DE BARRAS
87T	= RELÉ DIFERENCIAL DEL TRANSFORMADOR
89	= DESCONECTADOR
90	= REGULADOR DE VOLTAJE
CO	= CONTADOR DE OPERACIONES
If	= CORRIENTE DE FUGA
MR	= MULTIRRAZON
SC	= SWITCH CONTROL
BP	= BLOQUE DE PRUEBAS
FT	= SWITCH DE PRUEBAS
(BM)	= BLOQUEO MECÁNICO
(BE)	= BLOQUEO ELECTRO MECÁNICO
(P)	= LÁMPARA INDICADORA DE PRESENCIA DE TENSIÓN
	= RESISTENCIA DE PUESTA A TIERRA (FRG)
k_{NT}	= MEDICIÓN NORMA TÉCNICA
	= EQUIPO DE MEDIDA N.T DE DISTRIBUCIÓN.

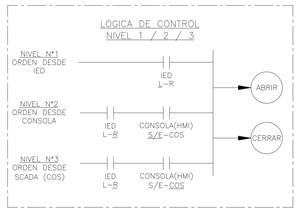

TRANSFORMADOR DE CORRIENTE MULTI RAZON TABLA 1							
600:5	50:5 100:5 150:5 200:5 250:5 300:5 400:5 450:5 500:5 600:5	1200:5	100:5 200:5 300:5 400:5 500:5 600:5 800:5 900:5 1000:5 1200:5	2000:5	300:5 400:5 500:5 800:5 1100:5 1200:5 1500:5 1600:5 2000:5	3000:5	300:5 500:5 800:5 1000:5 1200:5 1500:5 2000:5 2200:5 2500:5 3000:5

SEGUN NORMA ANSI/IEEE C57.13-1993

REFERENCIAS:

CHI-19468 DISPOSICIÓN GENERAL EQUIPO ELÉTRICO – PLANTA.
CHI-19469 DISPOSICIÓN GENERAL EQUIPO ELÉCTRICO – SECCIONES.

NOTAS:

1.– EL TAP CHACABUCO INICIALMENTE SE CONECTARA A LA LINEA DE 110 kV "CERRO NAVIA – LAS VEGAS" DE GENER.

ESTE DIAGRAMA UNILINEAL REEMPLAZA AL DIAGRAMA DEL MISMO NUMERO CHI-28931 LAMINA 1 REV. 0, DE FECHA 15.05.20 ((PROY.) NT DISTRIBUCIÓN)

SOCIEDAD TRANSMISORA METROPOLITANA S.A.

GERENCIA ZONAL DE TRANSMISIÓN METROPOLITANA

ÁREA DE INGENIERÍA Y PERMISOS

SUBESTACION CHACABUCO 110/23/12kV
DIAGRAMA UNILINEAL FUNCIONAL

N°	FECHA	MODIFICACIONES	PROY.	DIB.	REV.	APROB.
4	19.11.2024	CONEXIÓN NUEVO ALIMENTADOR ASCENTY A PAÑO E53	AINAMEN	AINAMEN	AINAMEN	H.B.N
3	30.07.2021	NUEVO TR4 50 MVA	IM.3	IM.3	N.V.S.	M.G.C.
2	30.07.2021	INSTALACIÓN TP CT5	IM.3	IM.3	N.V.S.	M.G.C.
1	30.07.2021	REUBICACIÓN TR4 A POSICIÓN TR5	IM.3	IM.3	N.V.S.	M.G.C.

UNIDAD APROB.	ESCALA: 1:1000	STM-19467	APROBADO
PROYECTÓ	IM.3		FECHA: 23.05.2023
DIBUJÓ	IM.3		STM-19467
REVISÓ	N. VÁSQUEZ S.		
ENCARGADO	M. GONZÁLEZ C.		
ENCARGADO DE UNIDAD	LÁMINA 7 DE 9		