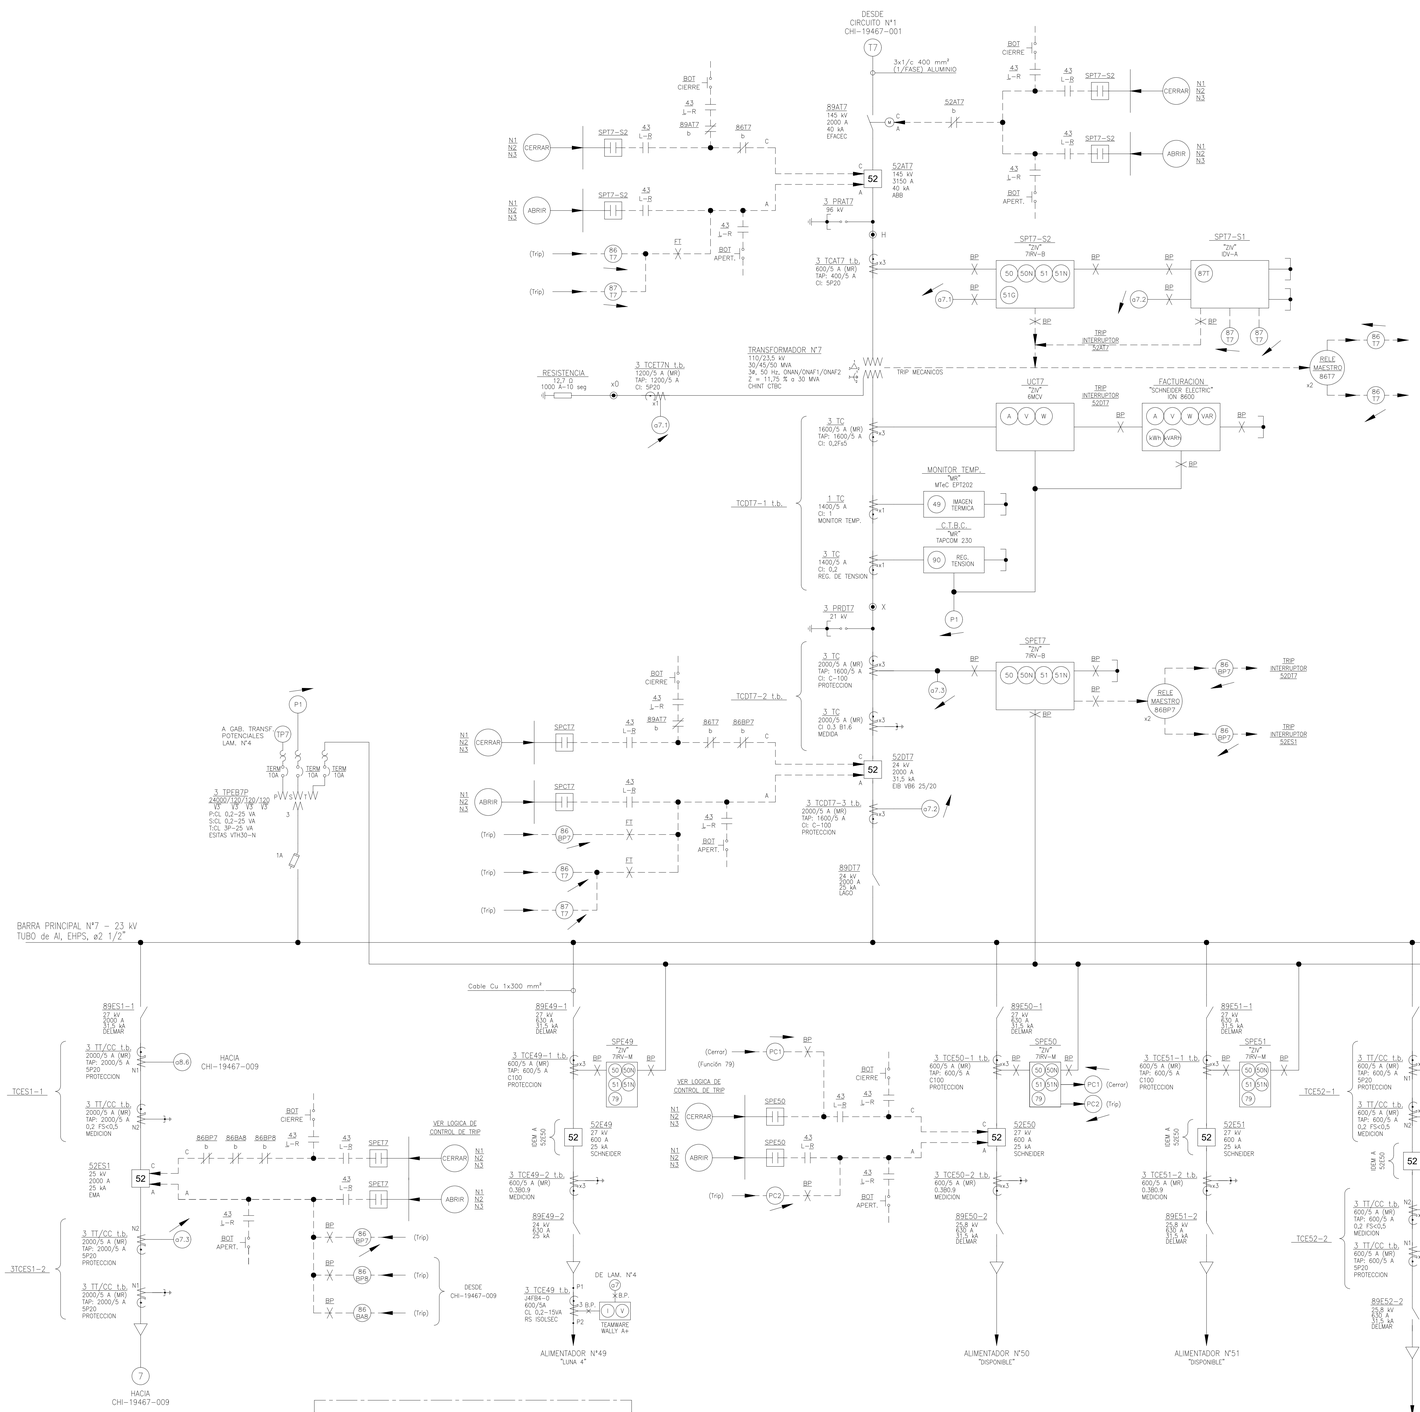


SIMBOLOGIA

A	: AMPERMETRO
A^T	: AMPERMETRO TERMICO
(I)	: INSTRUMENTOS
V	: VOLTMETRO
W	: WATTMETRO
(R)	: RELES
VAR	: VARMETRO
kWh	: MEDIDOR DE ENERGIA ACTIVA
M	: MOTORIZADO
-X-	: RELE DIFERENCIAL
-I-	: RELE SOBRE CORRIENTE DE FASE
-I-	: RELE SOBRE CORRIENTE RESIDUAL
-V-	: RELE BAJO VOLTAJE
-F-	: RELE BAJA FRECUENCIA
PS	: RELE PRESION SUBITA
MR	: MULTIRAZON
	: MUFA TRIFASICA 12KV
	: TERMINAL PARA CABLE EPR 240mm²
CTBC	: REGULADOR DE VOLTAJE CTBC
52	: INTERRUPTOR
	: TRANSFORMADOR DE PODER
	: CONEXION PAT
	: RESISTENCIA PAT
	: FASES CORTOCIRCUITADAS
	: FASES CORTOCIRCUITADAS Y PUESTA A TIERRA
	: PARARRAYOS SIN CONTADOR DE DESCARGA
3PR	: PARARRAYOS (OXIDO METALICO) CON CONTADOR DE DESCARGA
	: CODENSADOR DE ACOPLAMIENTO
	: TRANSFORMADOR DE POTENCIAL INDUCTIVO DE DOS DEVANADOS
	: TRANSFORMADOR DE POTENCIAL
	: TRANSFORMADOR DE CORRIENTE
	: TRANSFORMADOR DE CORRIENTE CON BUSHING
	: DESCONECTADOR MOTORIZADO CON CUCHILLA DE PUESTA A TIERRA (C/Pat.)
	: DESCONECTADOR MOTORIZADO sin PUESTA A TIERRA (S/Pat.)
	: DESCONECTADOR
	: DESCONECTADOR CON PAT MOTORIZADO

ESTE PLANO REEMPLAZA AL NUMERO CHI-28931 LAMINA 4 REV. 0. DE FECHA 15.05.20 ((PROY.) NT DISTRIBUCIÓN)

REFERENCIAS:

CHI-19468 DISPOSICIÓN GENERAL EQUIPO ELÉTRICO – PLANTA.
CHI-19469 DISPOSICIÓN GENERAL EQUIPO ELÉCTRICO – SECCIONES.

NOTAS:

1.– EL TAP CHACABUCO INICIALMENTE SE CONECTARA A LA LÍNEA DE 110 kV "CERRO NAVIA – LAS VEGAS" DE GENER.

TRANSFORMADOR DE CORRIENTE MULTI RAZON TABLA 1

600:5	50:5	1200:5	100:5	2000:5	300:5	3000:5	300:5
	100:5		200:5		400:5		500:5
	150:5		300:5		500:5		800:5
	200:5		400:5		800:5		1000:5
	250:5		500:5		1100:5		1200:5
	300:5		600:5		1200:5		1500:5
	400:5		800:5		1500:5		2000:5
	450:5		900:5		1600:5		2200:5
	500:5		1000:5		2000:5		2500:5
	600:5		1200:5				3000:5

SEGUN NORMA ANSI/IEEE C57.13-1993

SOCIEDAD TRANSMISORA METROPOLITANA S.A.
GERENCIA ZONAL DE TRANSMISIÓN METROPOLITANA
ÁREA DE INGENIERÍA Y PERMISOS
SUBESTACION CHACABUCO 110/23/12kV
DIAGRAMA UNILINEAL FUNCIONAL

Nº	FECHA	MODIFICACIONES	PROY	DIB.	REV.	APROB.
4	19.11.2024	CONEXIÓN NUEVO ALIMENTADOR ASCENTY A PAÑO E53	ANAMEN	ANAMEN	ANAMEN	H.B.N.
3	30.07.2021	NUEVO TR4 50 MVA	IM3	IM3	N.V.S.	M.G.C.
2	30.07.2021	INSTALACIÓN TP CT5	IM3	IM3	N.V.S.	M.G.C.
1	30.07.2021	REUBICACIÓN TR4 A POSICIÓN TR5	IM3	IM3	N.V.S.	M.G.C.

ESCALA: 1:1000 | STM-19467
PROYECTÓ IM3 | DIBUJÓ IM3 | REVISÓ N. VÁSQUEZ S. | ENCARGADO M. GONZÁLEZ C.
UNIDAD APROB. | ENCARGADO DE UNIDAD
APROBADO
FECHA: 23.05.2023
STM-19467
LÁMINA 8 DE 9