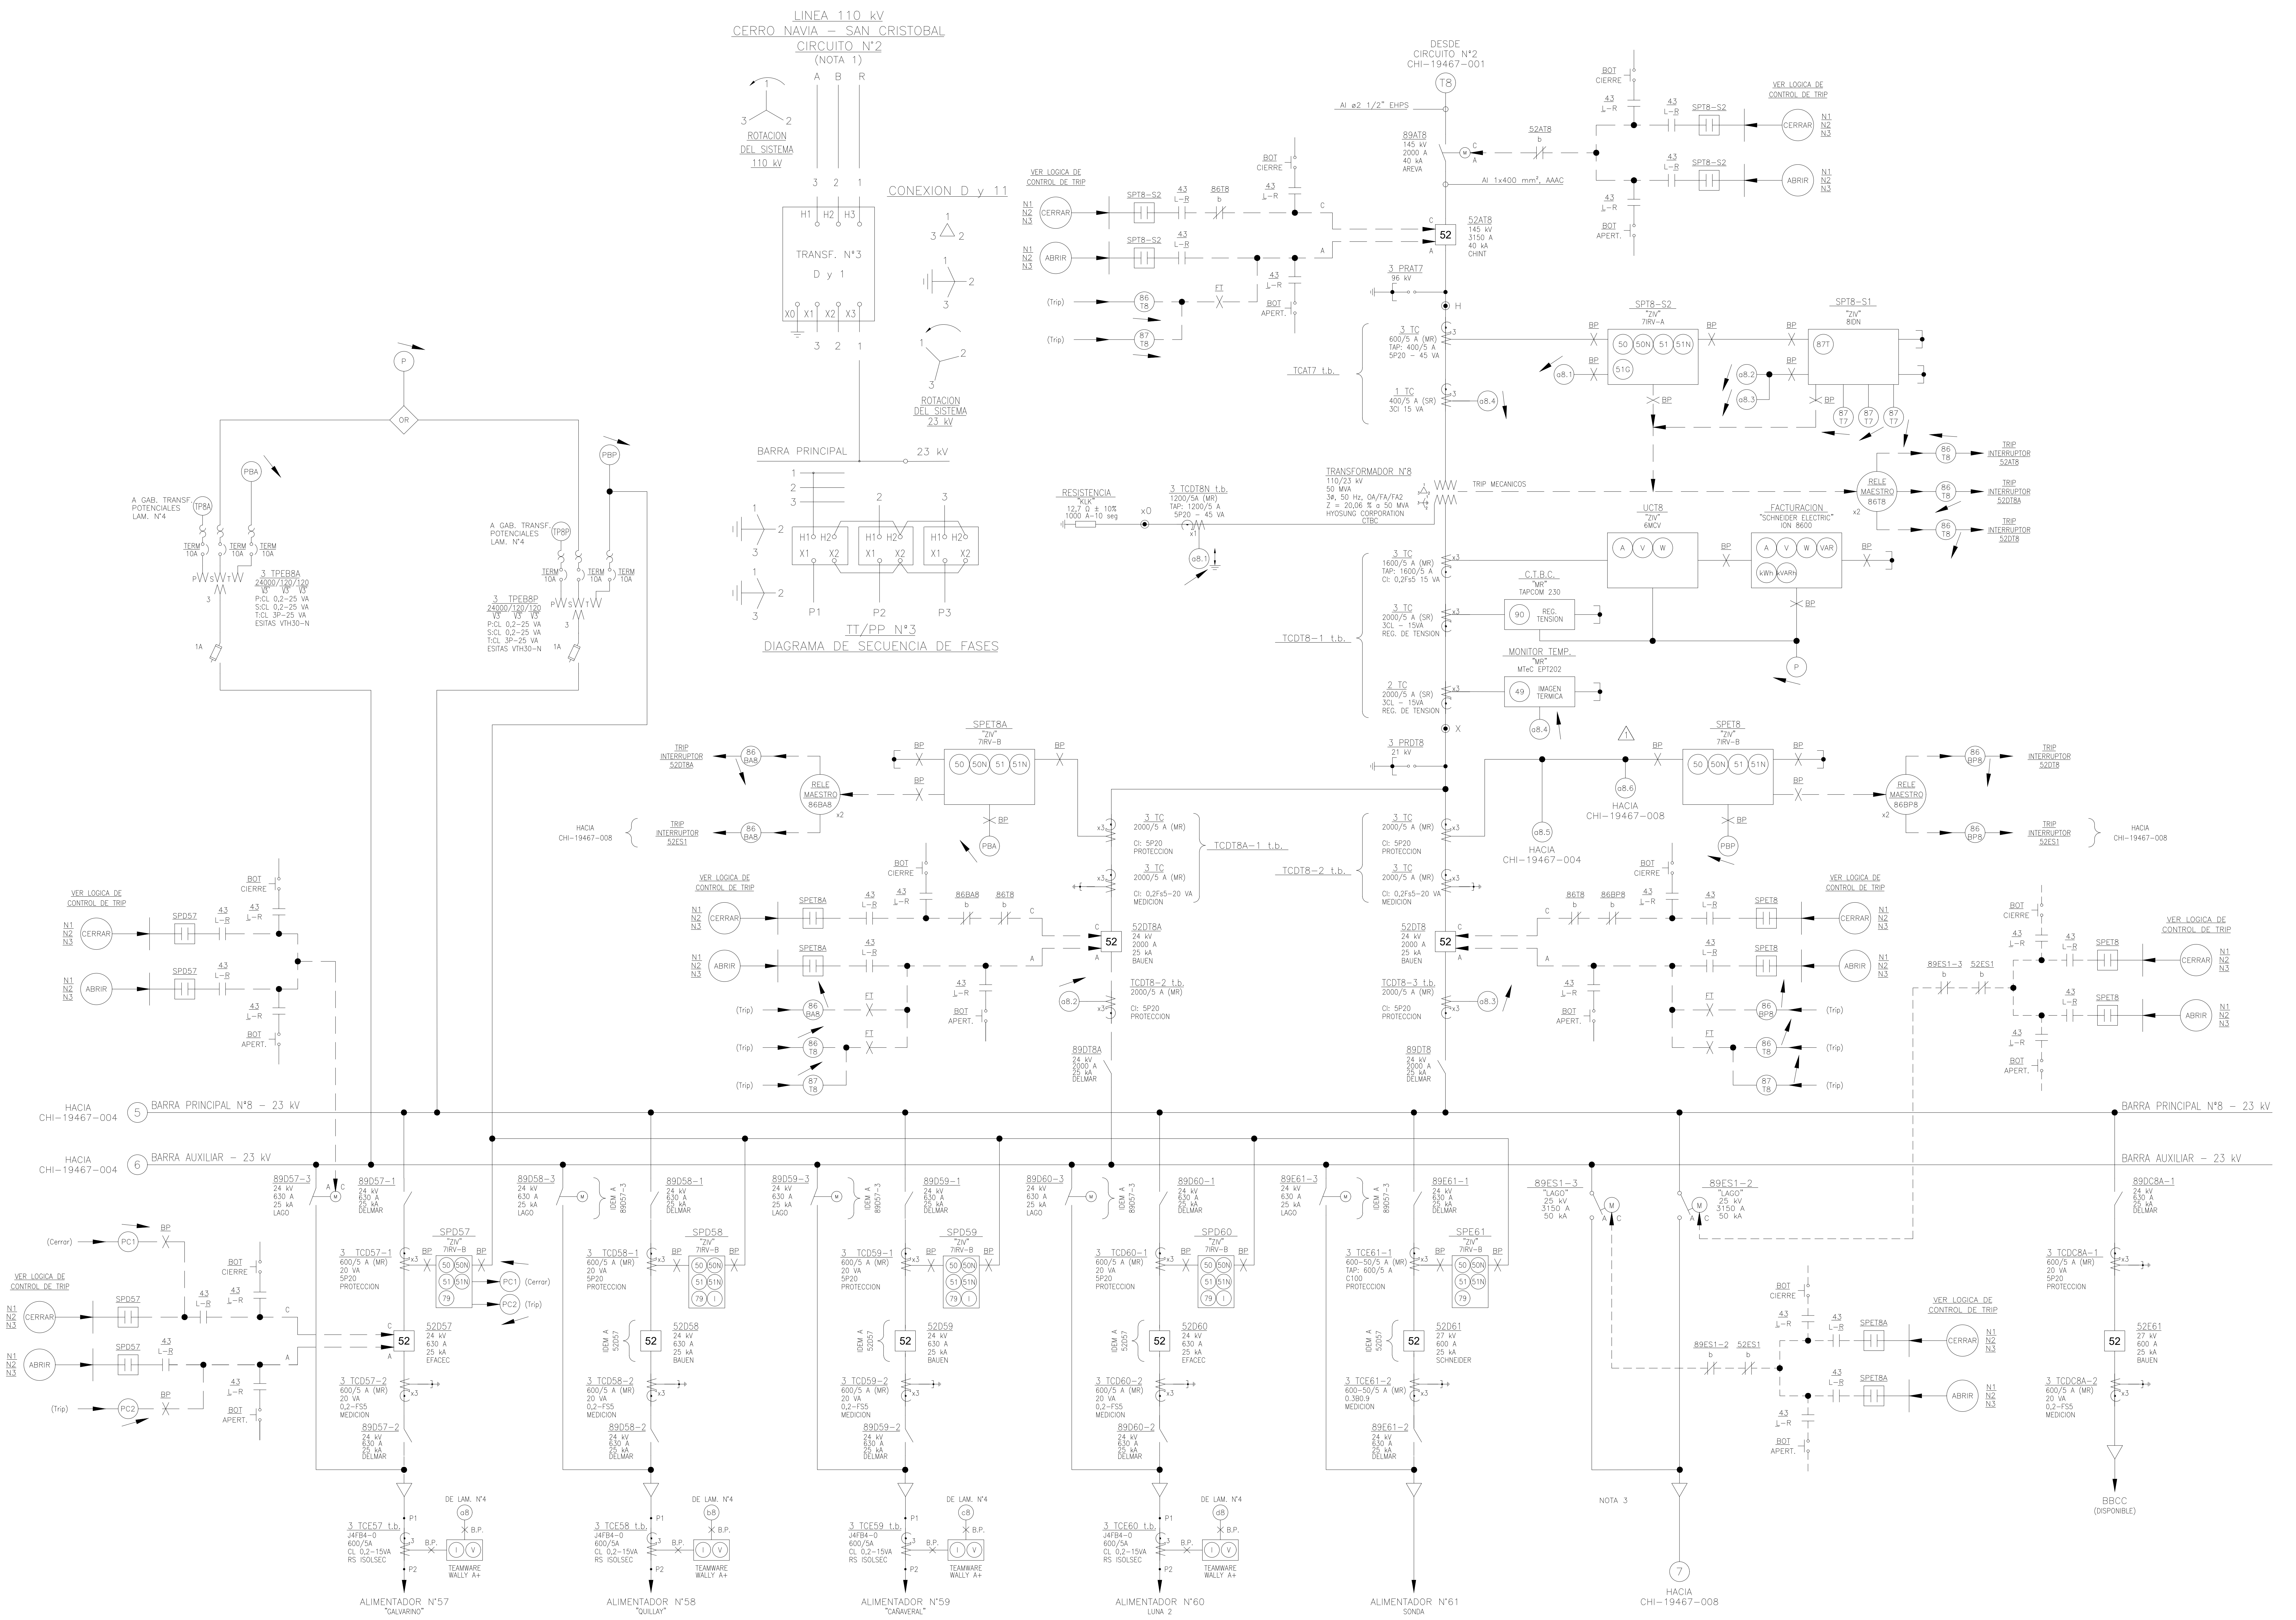

SIMBOLOGIA	
A	: AMPERMETRO
A^T	: AMPERMETRO TERMICO
Ⓘ	: INSTRUMENTOS
V	: VOLTMETRO
W	: WATTMETRO
Ⓡ	: RELES
VAR	: VARMETRO
kWh	: MEDIDOR DE ENERGIA ACTIVA
M	: MOTORIZADO
←X→	: RELE DIFERENCIAL
←→	: RELE SOBRE CORRIENTE DE FASE
⊢←→⊣	: RELE SOBRE CORRIENTE RESIDUAL
>—V—<	: RELE BAJO VOLTAJE
>—F—<	: RELE BAJA FRECUENCIA
←PS→	: RELE PRESION SUBITA
MR	: MULTIRAZON
↓	: MUFA TRIFASICA 12KV
↓	: TERMINAL PARA CABLE EPR 240mm²
Ⓡ CTBC	: REGULADOR DE VOLTAJE CTBC
52	: INTERRUPTOR
	: TRANSFORMADOR DE PODER
	: CONEXION PAT
	: RESISTENCIA PAT
	: FASES CORTOCIRCUITADAS
	: FASES CORTOCIRCUITADAS Y PUESTA A TIERRA
	: PARARRAYOS SIN CONTADOR DE DESCARGA
3PR	: PARARRAYOS (OXIDO METALICO) CON CONTADOR DE DESCARGA
	: CODENSADOR DE ACOPLAMIENTO
	: TRANSFORMADOR DE POTENCIAL INDUCTIVO DE DOS DEVANADOS
	: TRANSFORMADOR DE POTENCIAL
	: TRANSFORMADOR DE CORRIENTE
	: TRANSFORMADOR DE CORRIENTE CON BUSHING
M	: DESCONECTADOR MOTORIZADO CON CUCHILLA DE PUESTA A TIERRA (C/Pat)
	: DESCONECTADOR MOTORIZADO sin PUESTA A TIERRA (S/Pat)
	: DESCONECTADOR
M	: DESCONECTADOR CON PAT MOTORIZADO

REFERENCIAS:

CHI–19468 DISPOSICIÓN GENERAL EQUIPO ELÉTRICO – PLANTA.
CHI–19469 DISPOSICIÓN GENERAL EQUIPO ELÉCTRICO – SECCIONES.

NOTAS:

1.– EL TAP CHACABUCO INICIALMENTE SE CONECTARA A LA LÍNEA DE 110 kV "CERRO NAVÍA – LAS VEGAS" DE GENER.

2.– EL PATIO DE 23 kV SERA PROYECTADO CONSTRUIDO PARA 6 ALIMENTADORES Y 2 BANCOS DE CONDENSADORES PARA LA ETAPA FINAL DE UN TRANSFORMADOR DE 50 MVA.

3.– PARA LA IMPLEMENTACION DE LA INTERCONEXION CON BARRA N°7 SE UTILIZARA LA ACTUAL POSICION DEL ALIMENTADOR N°62, REEMPLAZANDO LOS DESCONECTADORES DISPONIBLES POR UNOS DE MAYOR CAPACIDAD.

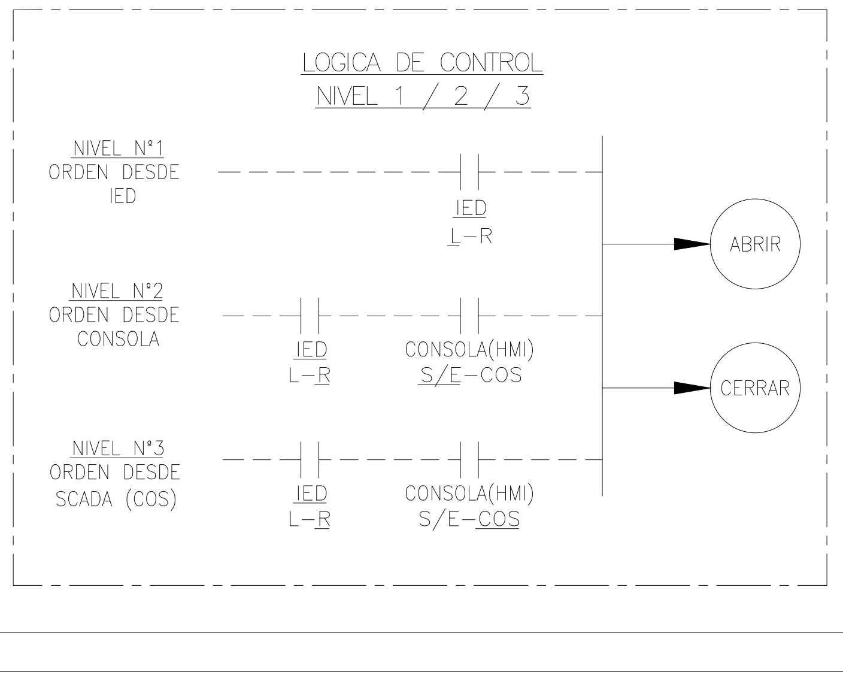

TRANSFORMADOR DE CORRIENTE MULTI RAZON						TABLA 1	
600:5	50:5 100:5 150:5 200:5 250:5 300:5 400:5 450:5 500:5 600:5	1200:5	100:5 200:5 300:5 400:5 500:5 600:5 800:5 900:5 1000:5 1200:5	2000:5	300:5 400:5 500:5 800:5 1100:5 1200:5 1500:5 1600:5 2000:5	3000:5	300:5 500:5 800:5 1000:5 1200:5 1500:5 2000:5 2200:5 2500:5 3000:5

SEGUN NORMA ANSI/IEEE C57.13–1993

ESTE PLANO REEMPLAZA AL NUMERO CHI–28931 LAMINA 3 REV. 0.
DE FECHA 15.05.20 ((PROY.) NT DISTRIBUCIÓN)

SOCIEDAD TRANSMISORA METROPOLITANA S.A.
GERENCIA ZONAL DE TRANSMISIÓN METROPOLITANA
ÁREA DE INGENIERÍA Y PERMISOS
SUBESTACION CHACABUCO 110/23/12kV
DIAGRAMA UNILINEAL FUNCIONAL

N°	FECHA	MODIFICACIONES	PROY	DIB.	REV.	APROB.
4	19.11.2024	CONEXIÓN NUEVO ALIMENTADOR ASCENTY A PAÑO E53	AINAWEN	AINAWEN	AINAWEN	H.B.N
3	30.07.2021	NUEVO TR4 50 MVA	IM3	IM3	N.V.S.	M.G.C.
2	30.07.2021	INSTALACIÓN TP CT5	IM3	IM3	N.V.S.	M.G.C.
1	30.07.2021	REUBICACIÓN TR4 A POSICIÓN TR5	IM3	IM3	N.V.S	M.G.C.

ESCALA: 1:1000 STM–19467
PROYECTÓ IM3
DIBUJÓ IM3
REVISÓ N. VÁSQUEZ S.
ENCARGADO M. GONZÁLEZ C.
UNIDAD APROB. UNIDAD APROB.

APROBADO
ENCARGADO DE UNIDAD

FECHA: 23.05.2023
STM–19467
LÁMINA 9 DE 9