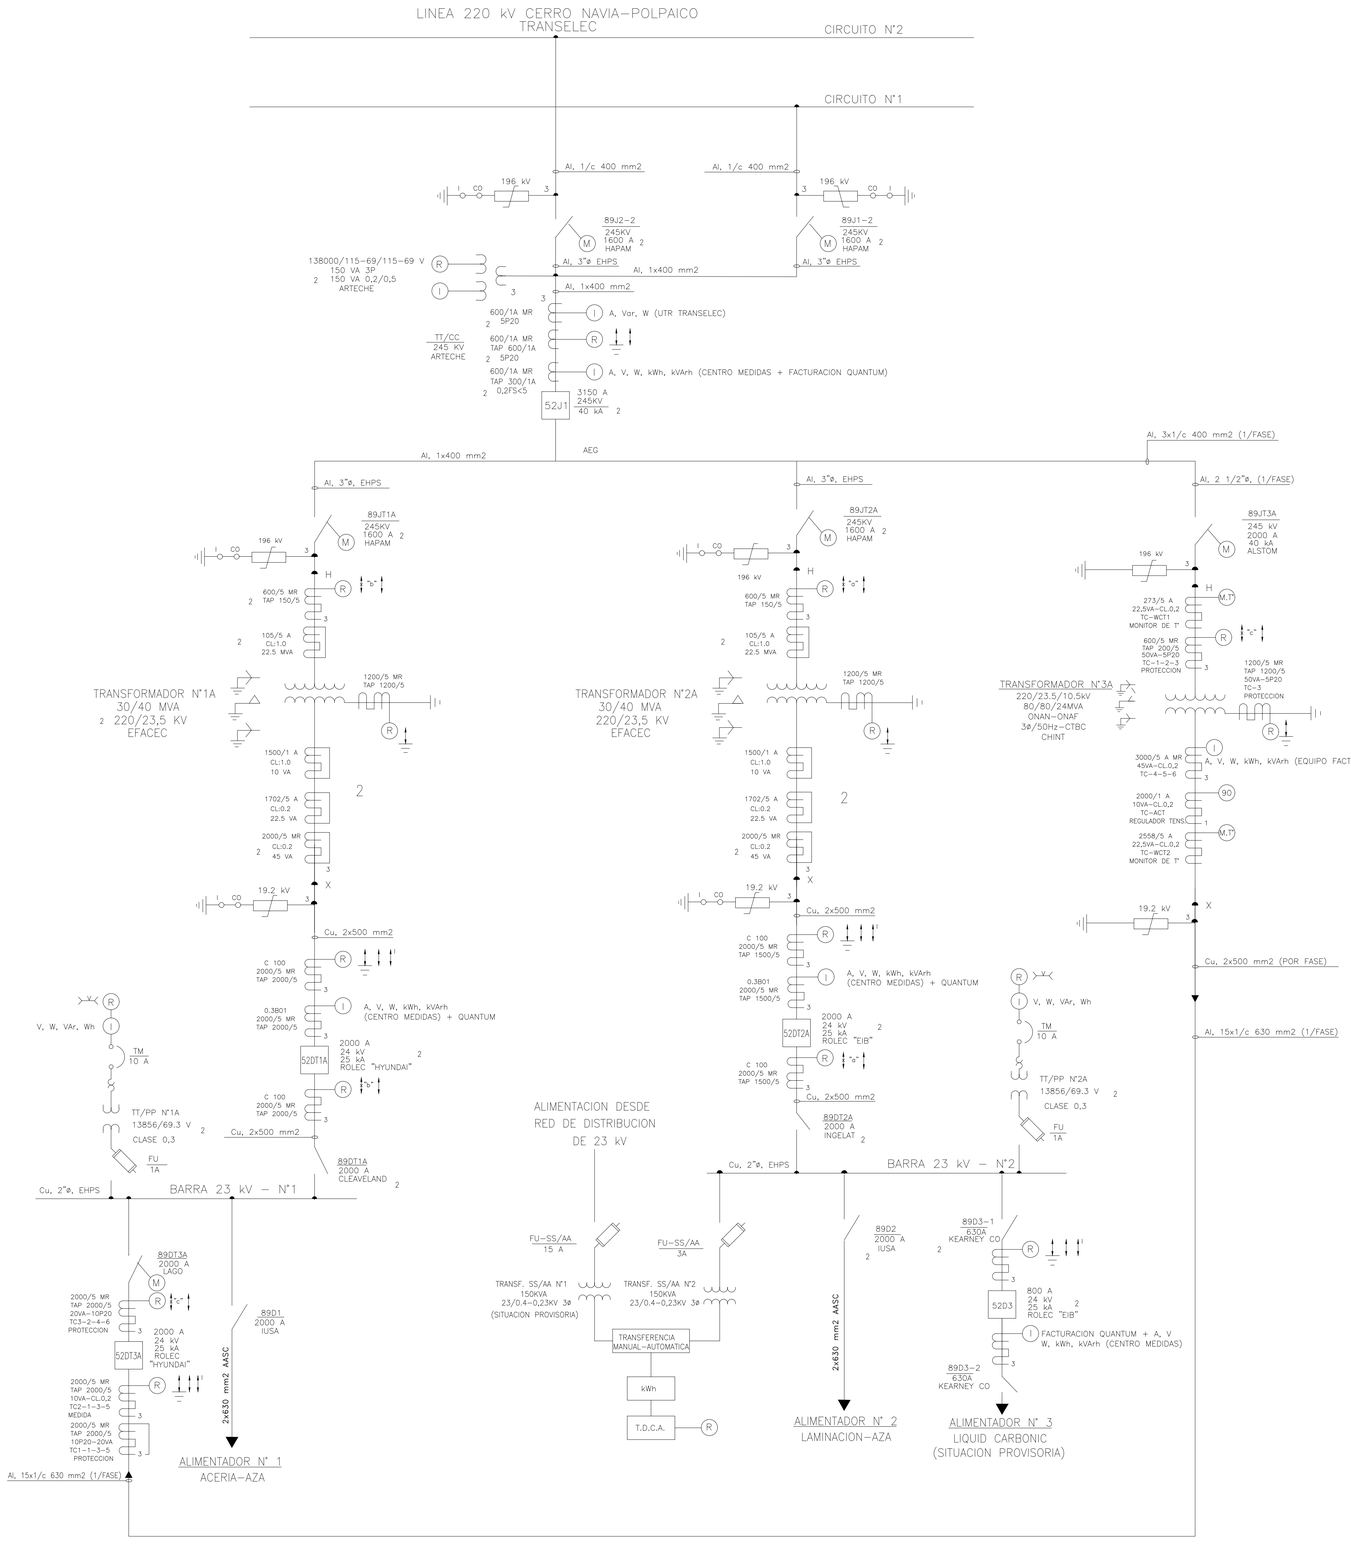


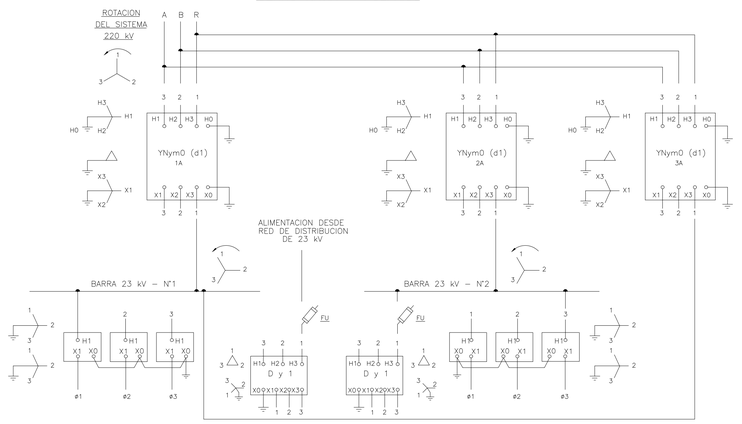




DIAGRAMA DE SECUENCIA DE FASES

## REFERENCIAS

| | |
|---|---|
| CHI – 19199 | DISPOSICION GENERAL EQUIPO ELECTRICO – PLANTA |
| CHI – 19200 | DISPOSICION GENERAL EQUIPO ELECTRICO – SECCIONES |
| CHI – 19203 | DISPOSICION GENERAL EQUIPO ELECTRICO – PATIO 23 kV |
| CHI – 19238 | DIAGRAMA FUNCIONAL |

## SIMBOLOGIA

- = RELE DIFERENCIAL
- = RELE DE SOBRECORRIENTE
- = RELE RESIDUAL
- = RELE SOBRECORRIENTE INSTANTANEO
- = RELE BAJO VOLTAJE

CAM CHILE SpA — EQUANS

EMITIDO PARA APROBACIÓN DEL CLIENTE

31.07.2024 REV: 11

SOCIEDAD TRANSMISORA METROPOLITANA II S.A.

GERENCIA ZONAL DE TRANSMISIÓN METROPOLITANA

ÁREA DE INGENIERÍA Y PERMISOS

S/E 220/23 kV LAMPA

DIAGRAMA UNILINEAL
FUNCIONAL

| N° | FECHA | MODIFICACIONES | PROY. | DIB. | REV. | APROBO |
|---|---|---|---|---|---|---|
| 5 | | | | | | |
| 4 | | | | | | |
| 3 | | | | | | |
| 2 | | | | | | |
| 1 | 03.07.23 | AMPLIACIÓN EN S/E NUEVA LAMPA (NTR ATMT) | CAM SpA | CAM SpA | J.C.C. | R.H.C. |

ESCALA: S/E — CEN171-0A21-CP-10-PLA-0011

PROYECTÓ: CAM SpA – EQUANS

DIBUJÓ: CAM SpA – EQUANS

REVISÓ: Soc.Transmisora Metropolitana II S.A.

ENCARGADO: LRR/CPM

UNIDAD APROB.: UIPyP&C/UICyP

ENCARGADO DE UNIDAD

APROBADO

FECHA: JUL. 2023

CHI-19201-001-L

LAMINA 1 DE 1