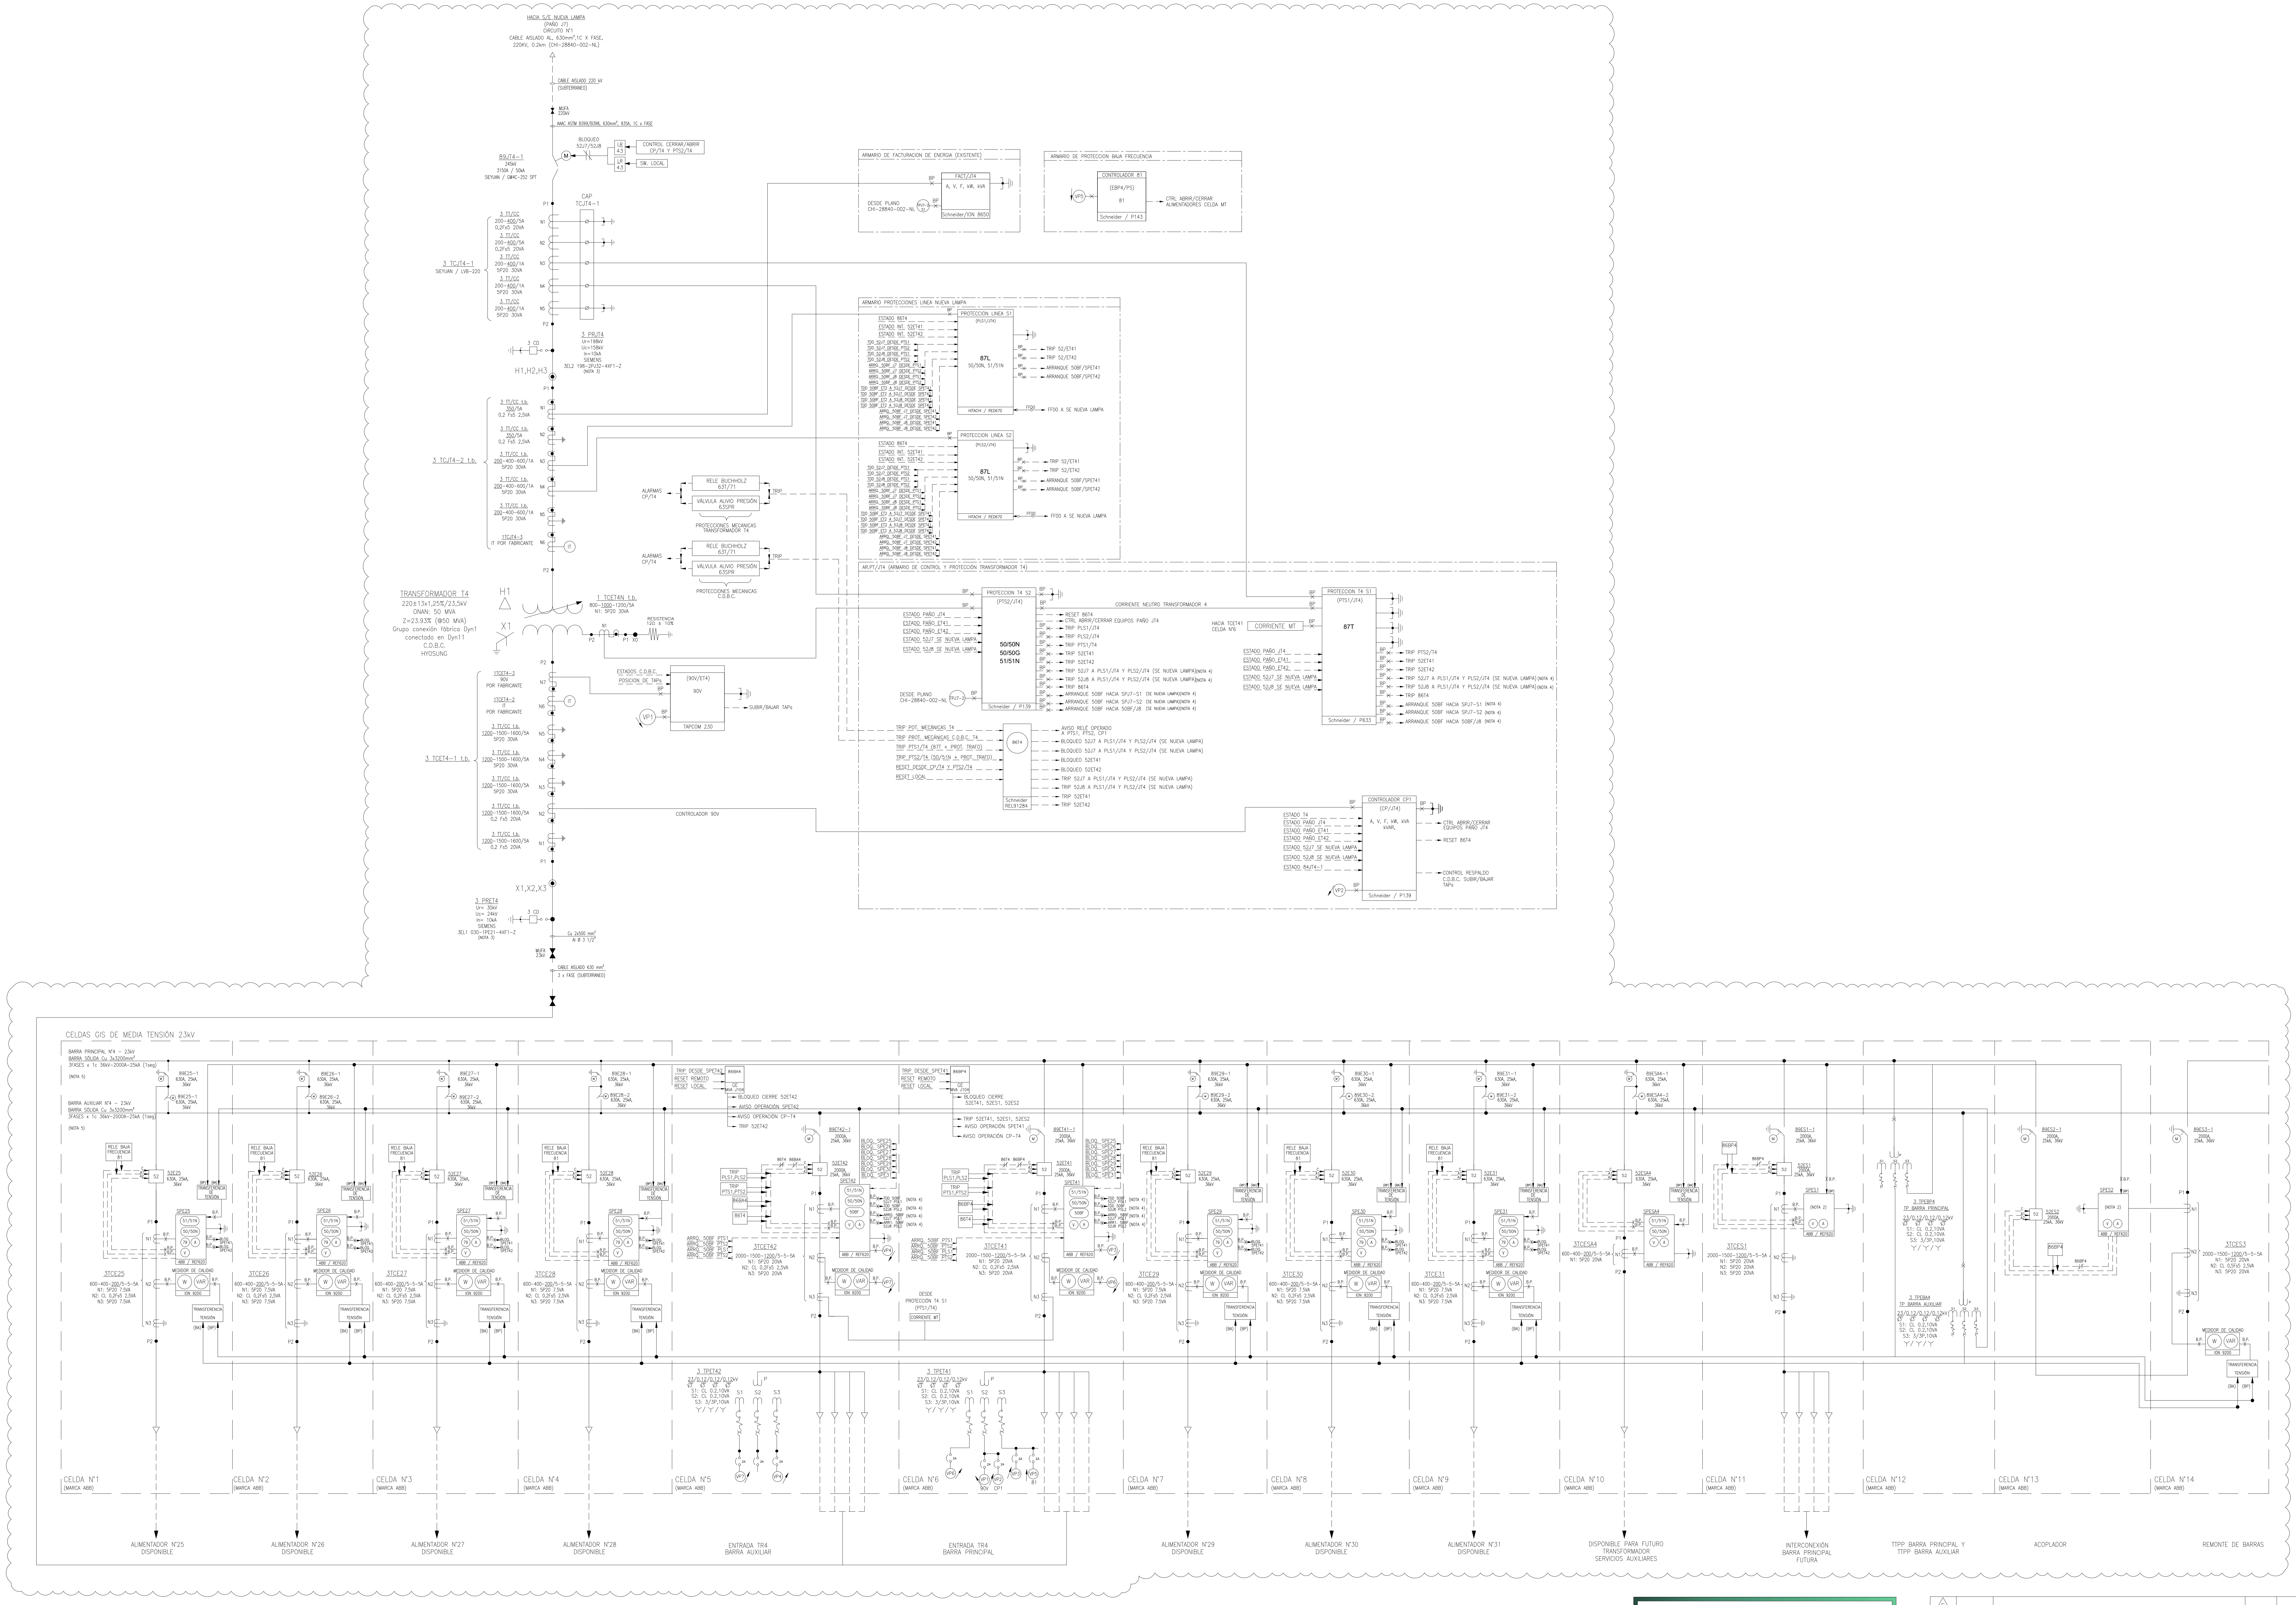

SIMBOLOGIA

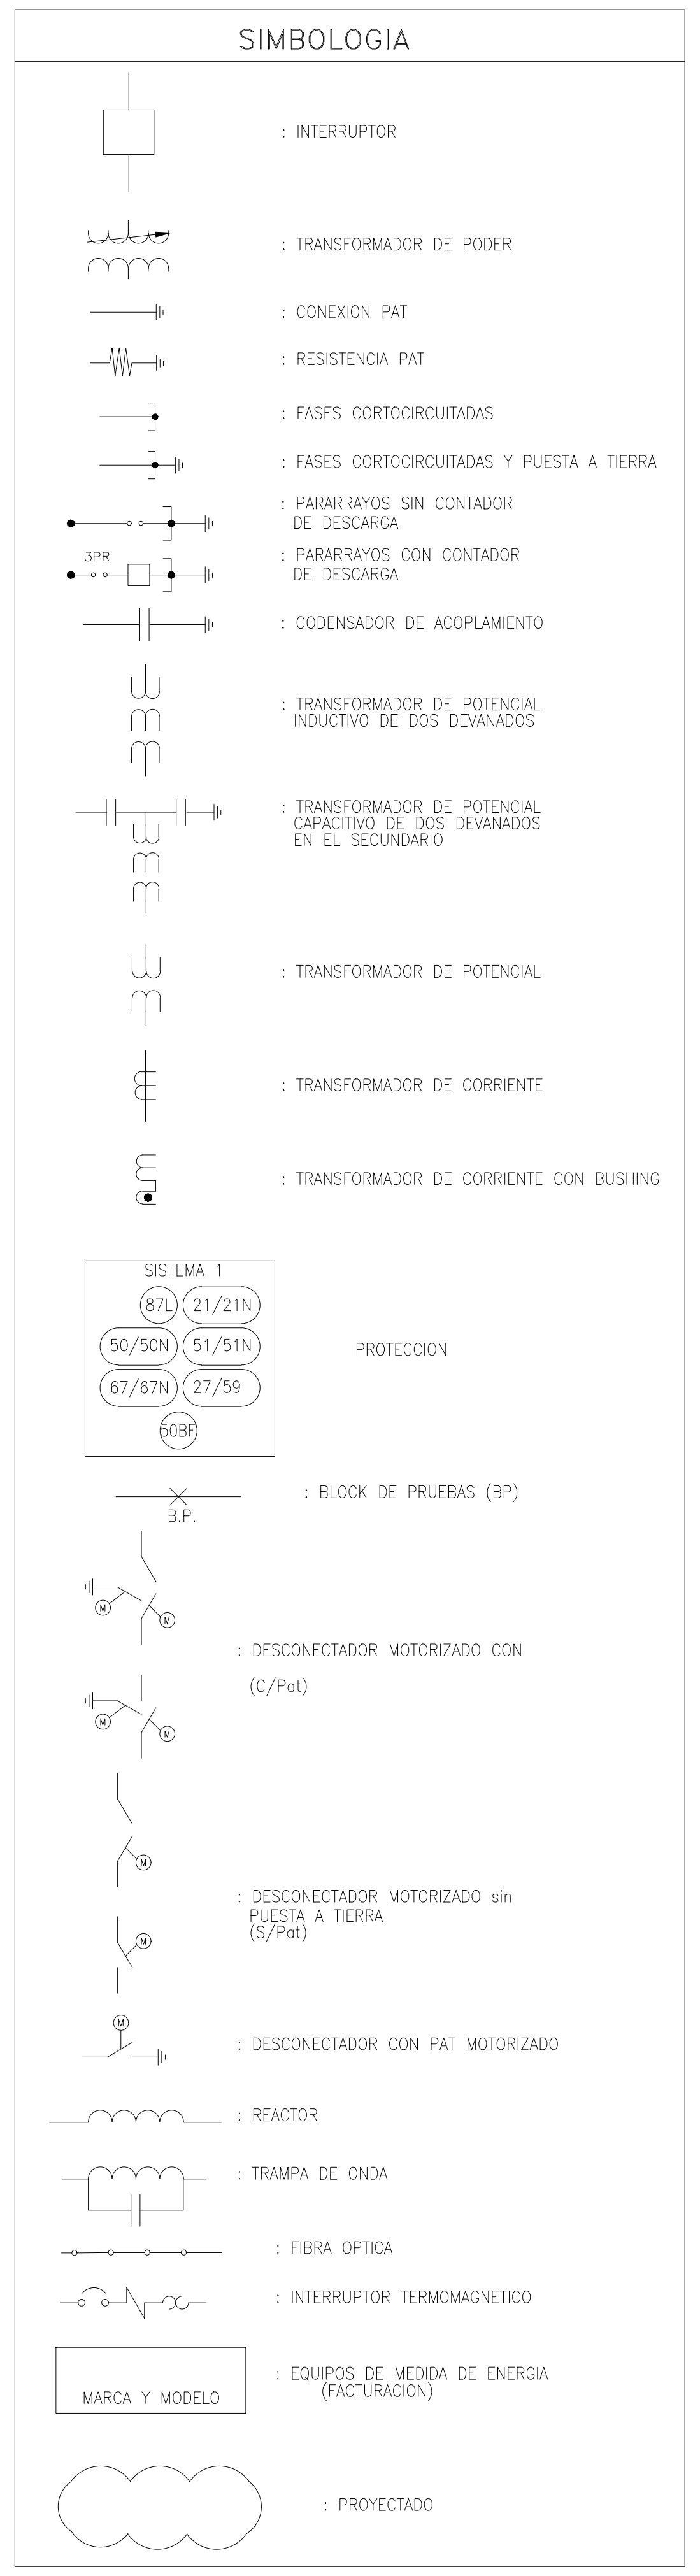
: INTERRUPTOR
: TRANSFORMADOR DE PODER
: CONEXION PAT
: RESISTENCIA PAT
: FASES CORTOCIRCUITADAS
: FASES CORTOCIRCUITADAS Y PUESTA A TIERRA
: PARARRAYOS SIN CONTADOR DE DESCARGA
3PR
: PARARRAYOS CON CONTADOR DE DESCARGA
: CODENSADOR DE ACOPLAMIENTO
: TRANSFORMADOR DE POTENCIAL INDUCTIVO DE DOS DEVANADOS
: TRANSFORMADOR DE POTENCIAL CAPACITIVO DE DOS DEVANADOS EN EL SECUNDARIO
: TRANSFORMADOR DE POTENCIAL
: TRANSFORMADOR DE CORRIENTE
: TRANSFORMADOR DE CORRIENTE CON BUSHING
SISTEMA 1
87L
21/21N
50/50N
51/51N
67/67N
27/59
50BF
PROTECCION
B.P.
: BLOCK DE PRUEBAS (BP)
: DESCONECTADOR MOTORIZADO CON (C/Pat)
: DESCONECTADOR MOTORIZADO sin PUESTA A TIERRA (S/Pat)
: DESCONECTADOR CON PAT MOTORIZADO
: REACTOR
: TRAMPA DE ONDA
: FIBRA OPTICA
: INTERRUPTOR TERMOMAGNETICO
MARCA Y MODELO
: EQUIPOS DE MEDIDA DE ENERGIA (FACTURACION)
: PROYECTADO

REFERENCIAS

CHI-19201-L	DIAGRAMA UNILINEAL SIMPLIFICADO
CHI-19199-L	DISPOSICIÓN DE EQUIPOS EN PATIO - PLANTA
CHI-19200-L	DISPOSICIÓN DE EQUIPOS EN PATIO - SECCIONES
CHI-32517-L	DISPOSICIÓN GRAL. EQUIPOS EN SALA DE CELDAS - PLANTA Y CORTES

NOTAS: (PROYECTO DE AMPLIACIÓN DE171/2020)

1. TODOS LOS EQUIPOS DEBEN SER CONFIRMADOS EN ESTA ETAPA DE LA INGENIERÍA, CONSIDERADO: MARCA, MODELO, DATOS TÉCNICOS.
2. EQUIPO NO REQUIERE FUNCIONES DE PROTECCIÓN.
3. LOS PARARRAYOS HACEN PARTE DEL SUMINISTRPO DEL TRANSFORMADOR DE PODER.
4. SE REALIZARÁ POR EL ENLACE DE COMUNICACIONES DE LAS PROTECCIONES DIFERENCIAL DE LINEA RED670
5. EL SUMINISTRO DE LAS CELDAS ES DE CLASE 36Kv PARA CUMPLIR CON LAS TENSIONES Y CLASES DE AISLACION INDICADAS EN LOS RPTD N° Y N°5, LA CUAL SERÁ ENERGIZADA EN 23kV.

CAM CHILE SpA
EQUANS
EMITIDO PARA APROBACIÓN DEL CLIENTE
31.07.2024 REV: 11

SOCIEDAD TRANSMISORA METROPOLITANA II S.A.
GERENCIA ZONAL DE TRANSMISIÓN METROPOLITANA
ÁREA DE INGENIERÍA Y PERMISOS

S/E 220/23 kV LAMPA

DIAGRAMA UNILINEAL FUNCIONAL

N°	FECHA	MODIFICACIONES	PROY.	DIB.	REV.	APROBO
5						
4						
3						
2						
1	11.05.23	AMPLIACIÓN EN S/E NUEVA LAMPA (NTR ATMT)	CAM SpA	CAM SpA	J.G.C.	R.H.G.

ESCALA: S/E	CEN171-0A21-CP-10-PLA-0011	APROBADO
PROYECTŌ	CAM SpA - EQUANS	
DIBUJŌ	CAM SpA - EQUANS	
REVISŌ	Soc.Transmisora Metropolitana II S.A.	
ENCARGADO	LRR/CPM	
UNIDAD APROB.	UIPyP&C/UICyP	ENCARGADO DE UNIDAD

FECHA: MAR. 2023
CHI-19201-002-L
LAMINA 2 DE 2